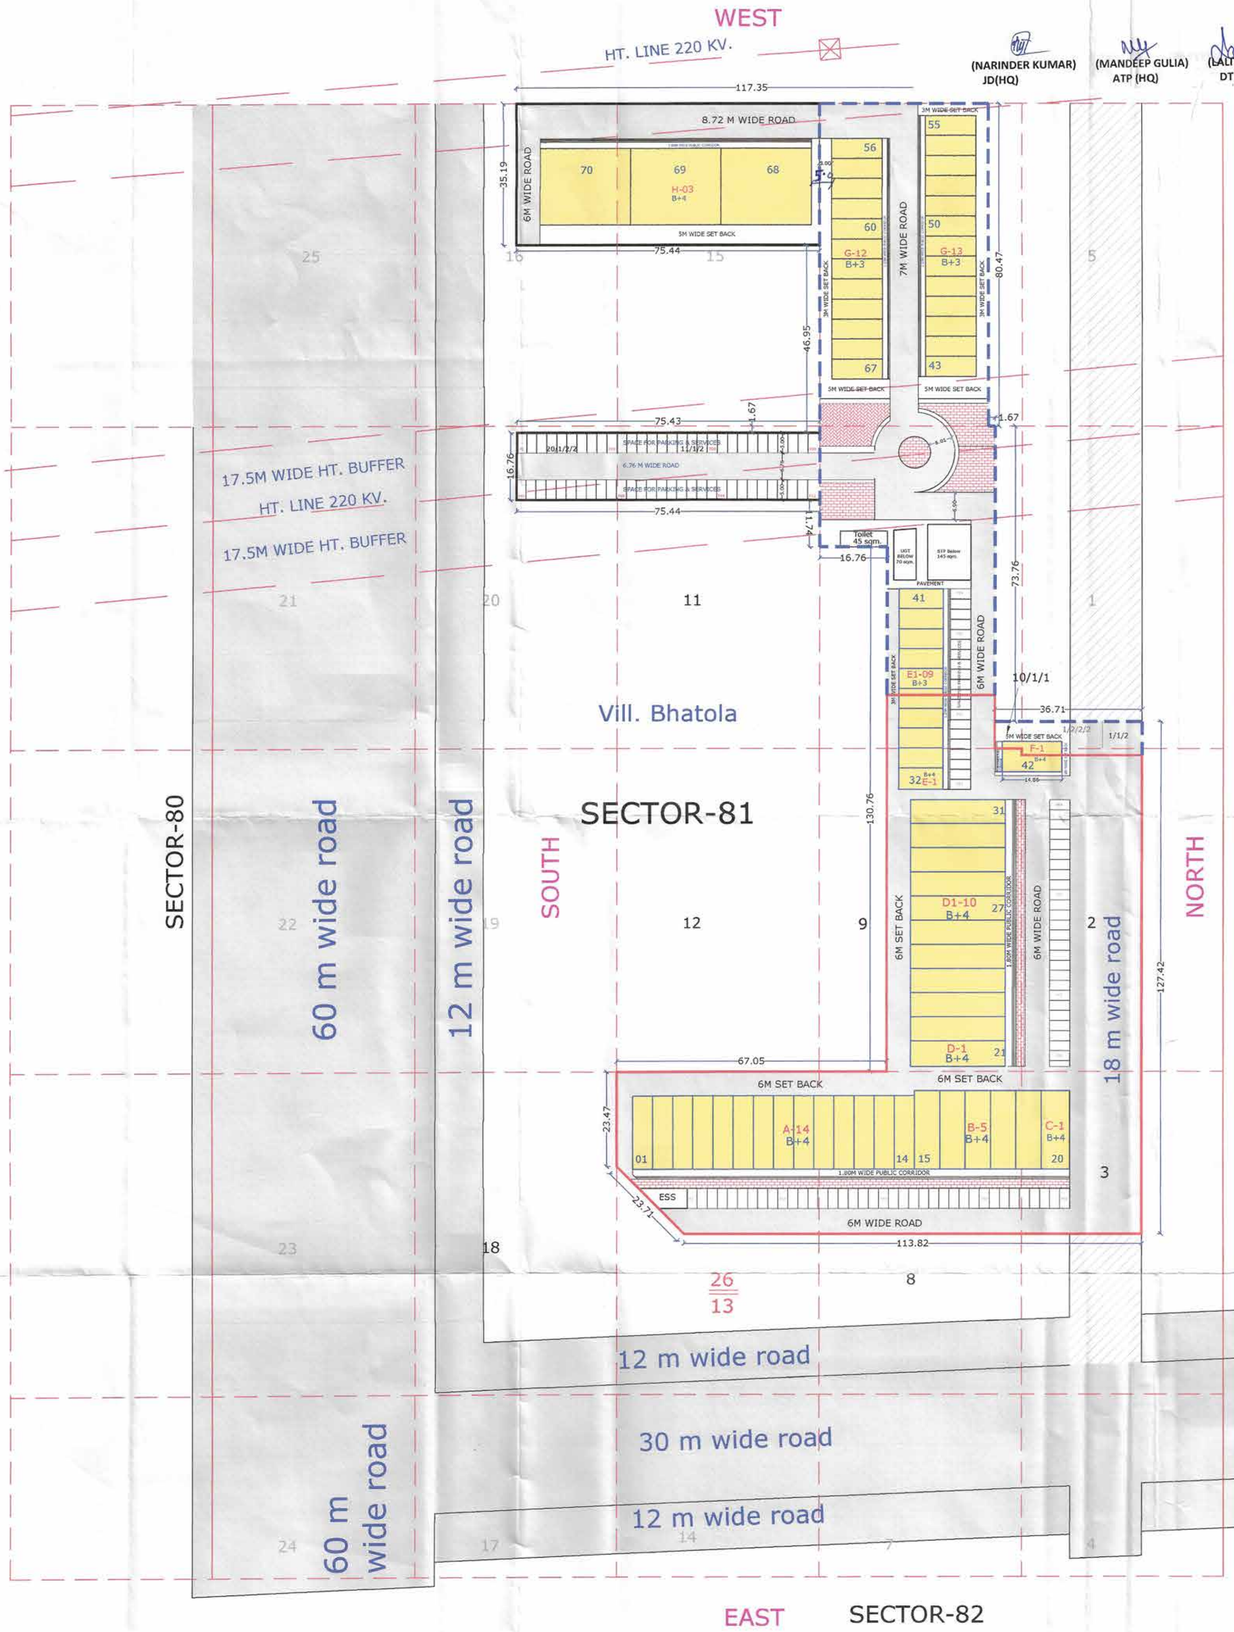

DESCRIPTION OF TOTAL AREA

Ⓐ ALREADY LICENCE GRANTED AREA FOR COMMERCIAL PLOTTED COLONY AREA- 2.606 acs.
(LICENCE no. 05 OF 2021) DT. 02.03.2021.

Ⓑ ALREADY ADDITIONAL AREA APPLIED FOR LICENCE OF COMMERCIAL PLOTTED COLONY/SCO. AREA MEASURING 1.475 acs.

Ⓒ ADDITIONAL AREA APPLIED FOR LICENCE OF COMMERCIAL PLOTTED COLONY/SCO. AREA MEASURING 0.96875 acs.

TOTAL AREA - A+B+C = 5.04975 ACS.

AREA STATEMENT :

DESCRIPTION	AREA IN SQ.METER	AREA IN ACRES
TOTAL AREA OF THE SCHEME	20435.58	5.04975 ACS.
PERMISSIBLE FAR = 150 %	30653.37 sqm.	7.574625 ACS.
PROPOSED FAR = 128.72%	26307.30 sqm.	6.50 ACS.
PERMISSIABLE GROUND COVERAGE	35.00% (7152.40 sqm.)	1.7674 ACS.
PROPOSED GROUND COVERAGE	34.78% (7108.18 sqm.)	1.7564 ACS.

AREA DETAIL

AREA DETAIL

TYPE OF PLOTS	PLOT NO.	DIMENSION OF PLOTS IN SQM. W	D	AREA OF PLOTS IN SQM.	NO OF PLOTS	NO. OF FLOOR	GROUND COVERAGE in sqm.	Total Units	Total FAR
A	01 to 14	5.00	18.21	91.05	14	4	1274.70	56	5098.8
B	15 to 19	6.30	19.39	122.16	5	4	610.79	20	2443.14
C	20	7.08	19.39	137.28	1	4	137.28	4	549.1248
D	21	6.47	23.52	152.17	1	4	152.17	4	608.6976
D1	22 to 31	6.00	23.52	141.12	10	4	1411.20	40	5644.8
E	32	5.33	10.97	58.47	1	3	58.47	3	175.4103
E1	33 to 41	4.97	10.97	54.52	9	3	490.69	27	1472.0643
F	42	7.53	14.86	111.90	1	4	111.90	4	447.5832
G	43 to 67	5.00	12.61	63.05	25	3	1576.25	75	4728.75
H	68 to 70	22.48	19.05	428.24	3	4	1284.73	12	5138.928
TOTAL.					70		7108.18	245	26307.30

Car Parking Size =2.5 X 5.0 meter = 12.50 @ ECS.

NOTE:PARKING AREA CANNOT BE SOLD IN ANY MANNER

Signature of Architect
SEEMA RANI
CA/2015/72259

ARCHITECT SIGNATURE

For Amolik Buildcon LLP
Auth. Signatory

AUTHORIZED SIGNATORY

SCALE 1 : 750

CLIENT:-
M/S AMOLIK BUILDCON LLP.
ADD. 14/3 MAIN MATHURA ROAD, MEWLA MAHARAJPUR, FARIDABAD HARYANA- 121003.

REVISED LAYOUT PLAN OF COMMERCIAL PLOTTED COLONY/ SCO IN SECTOR-81, AREA MEASURING - 5.04975 ACS. IN VILLAGE BHATOLA DISTRICT-FARIDABAD, HARYANA.

DATE:- FEB-2023

DESIGN BY:-PANKAJ KAPOOR (8800093157)